

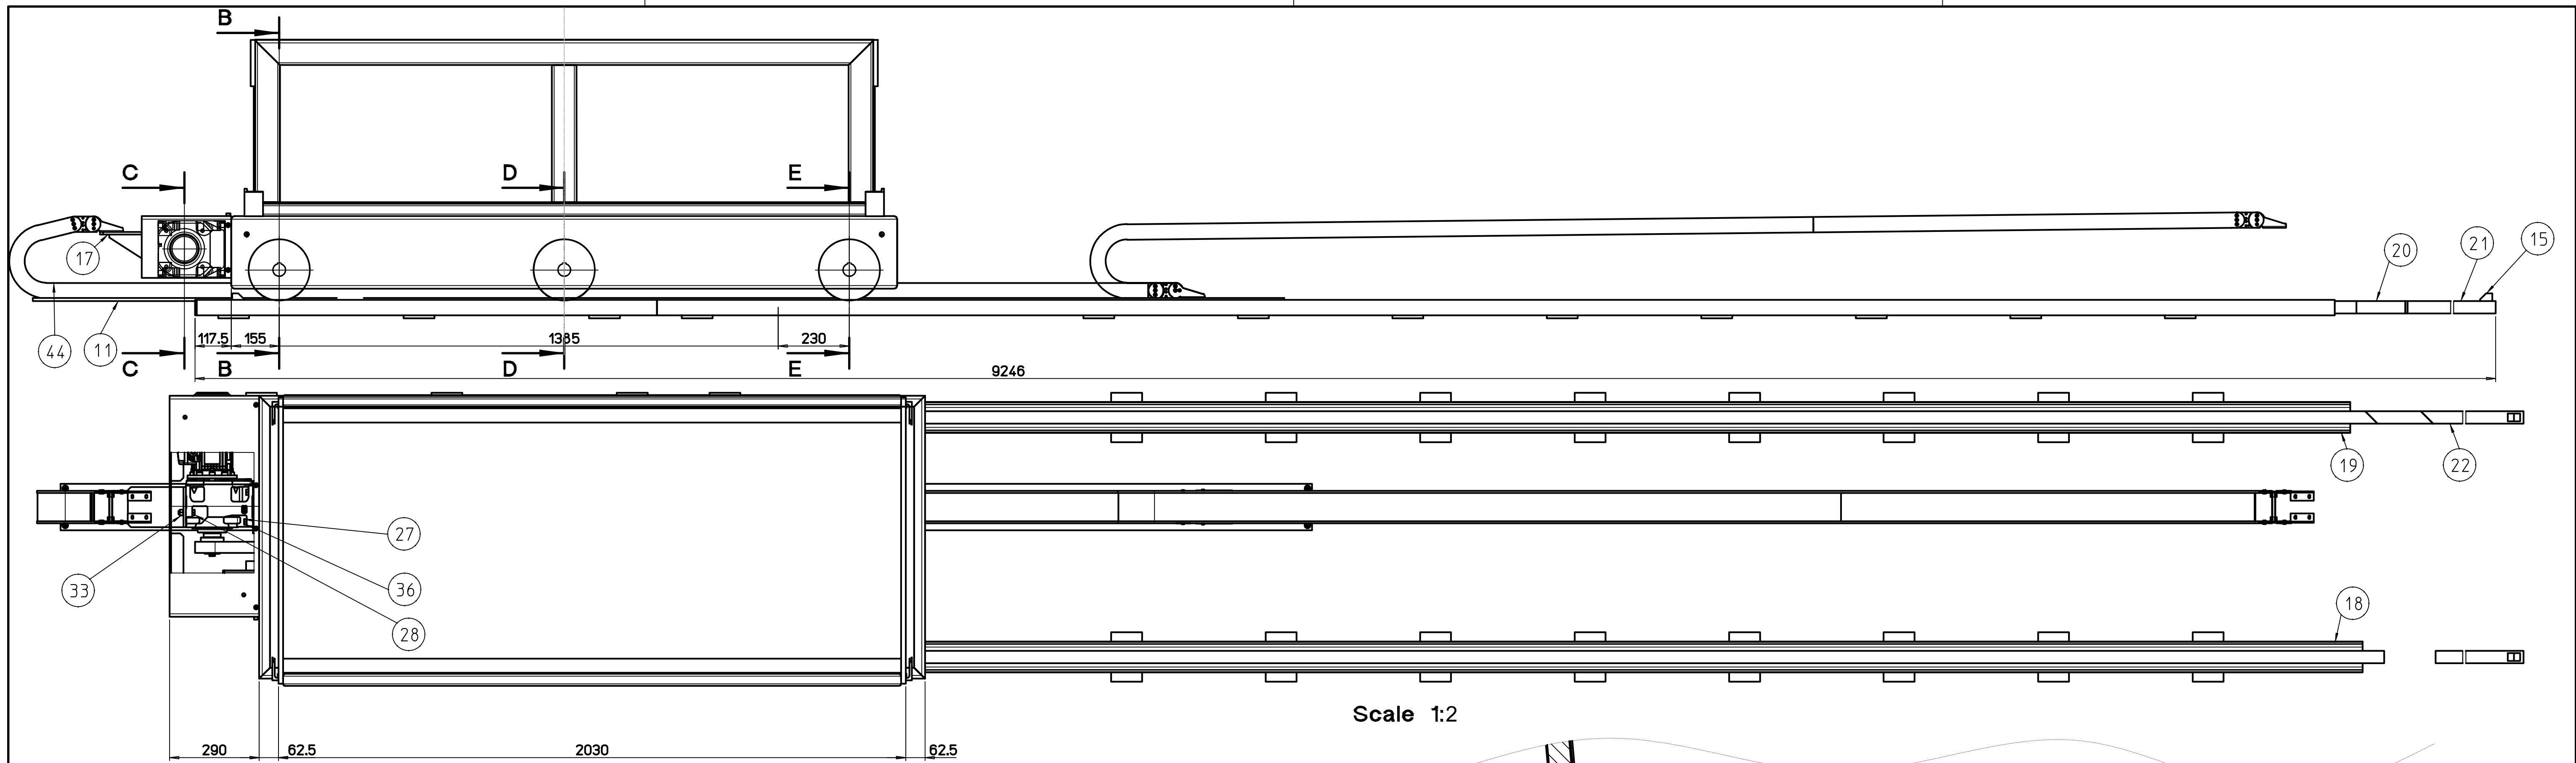
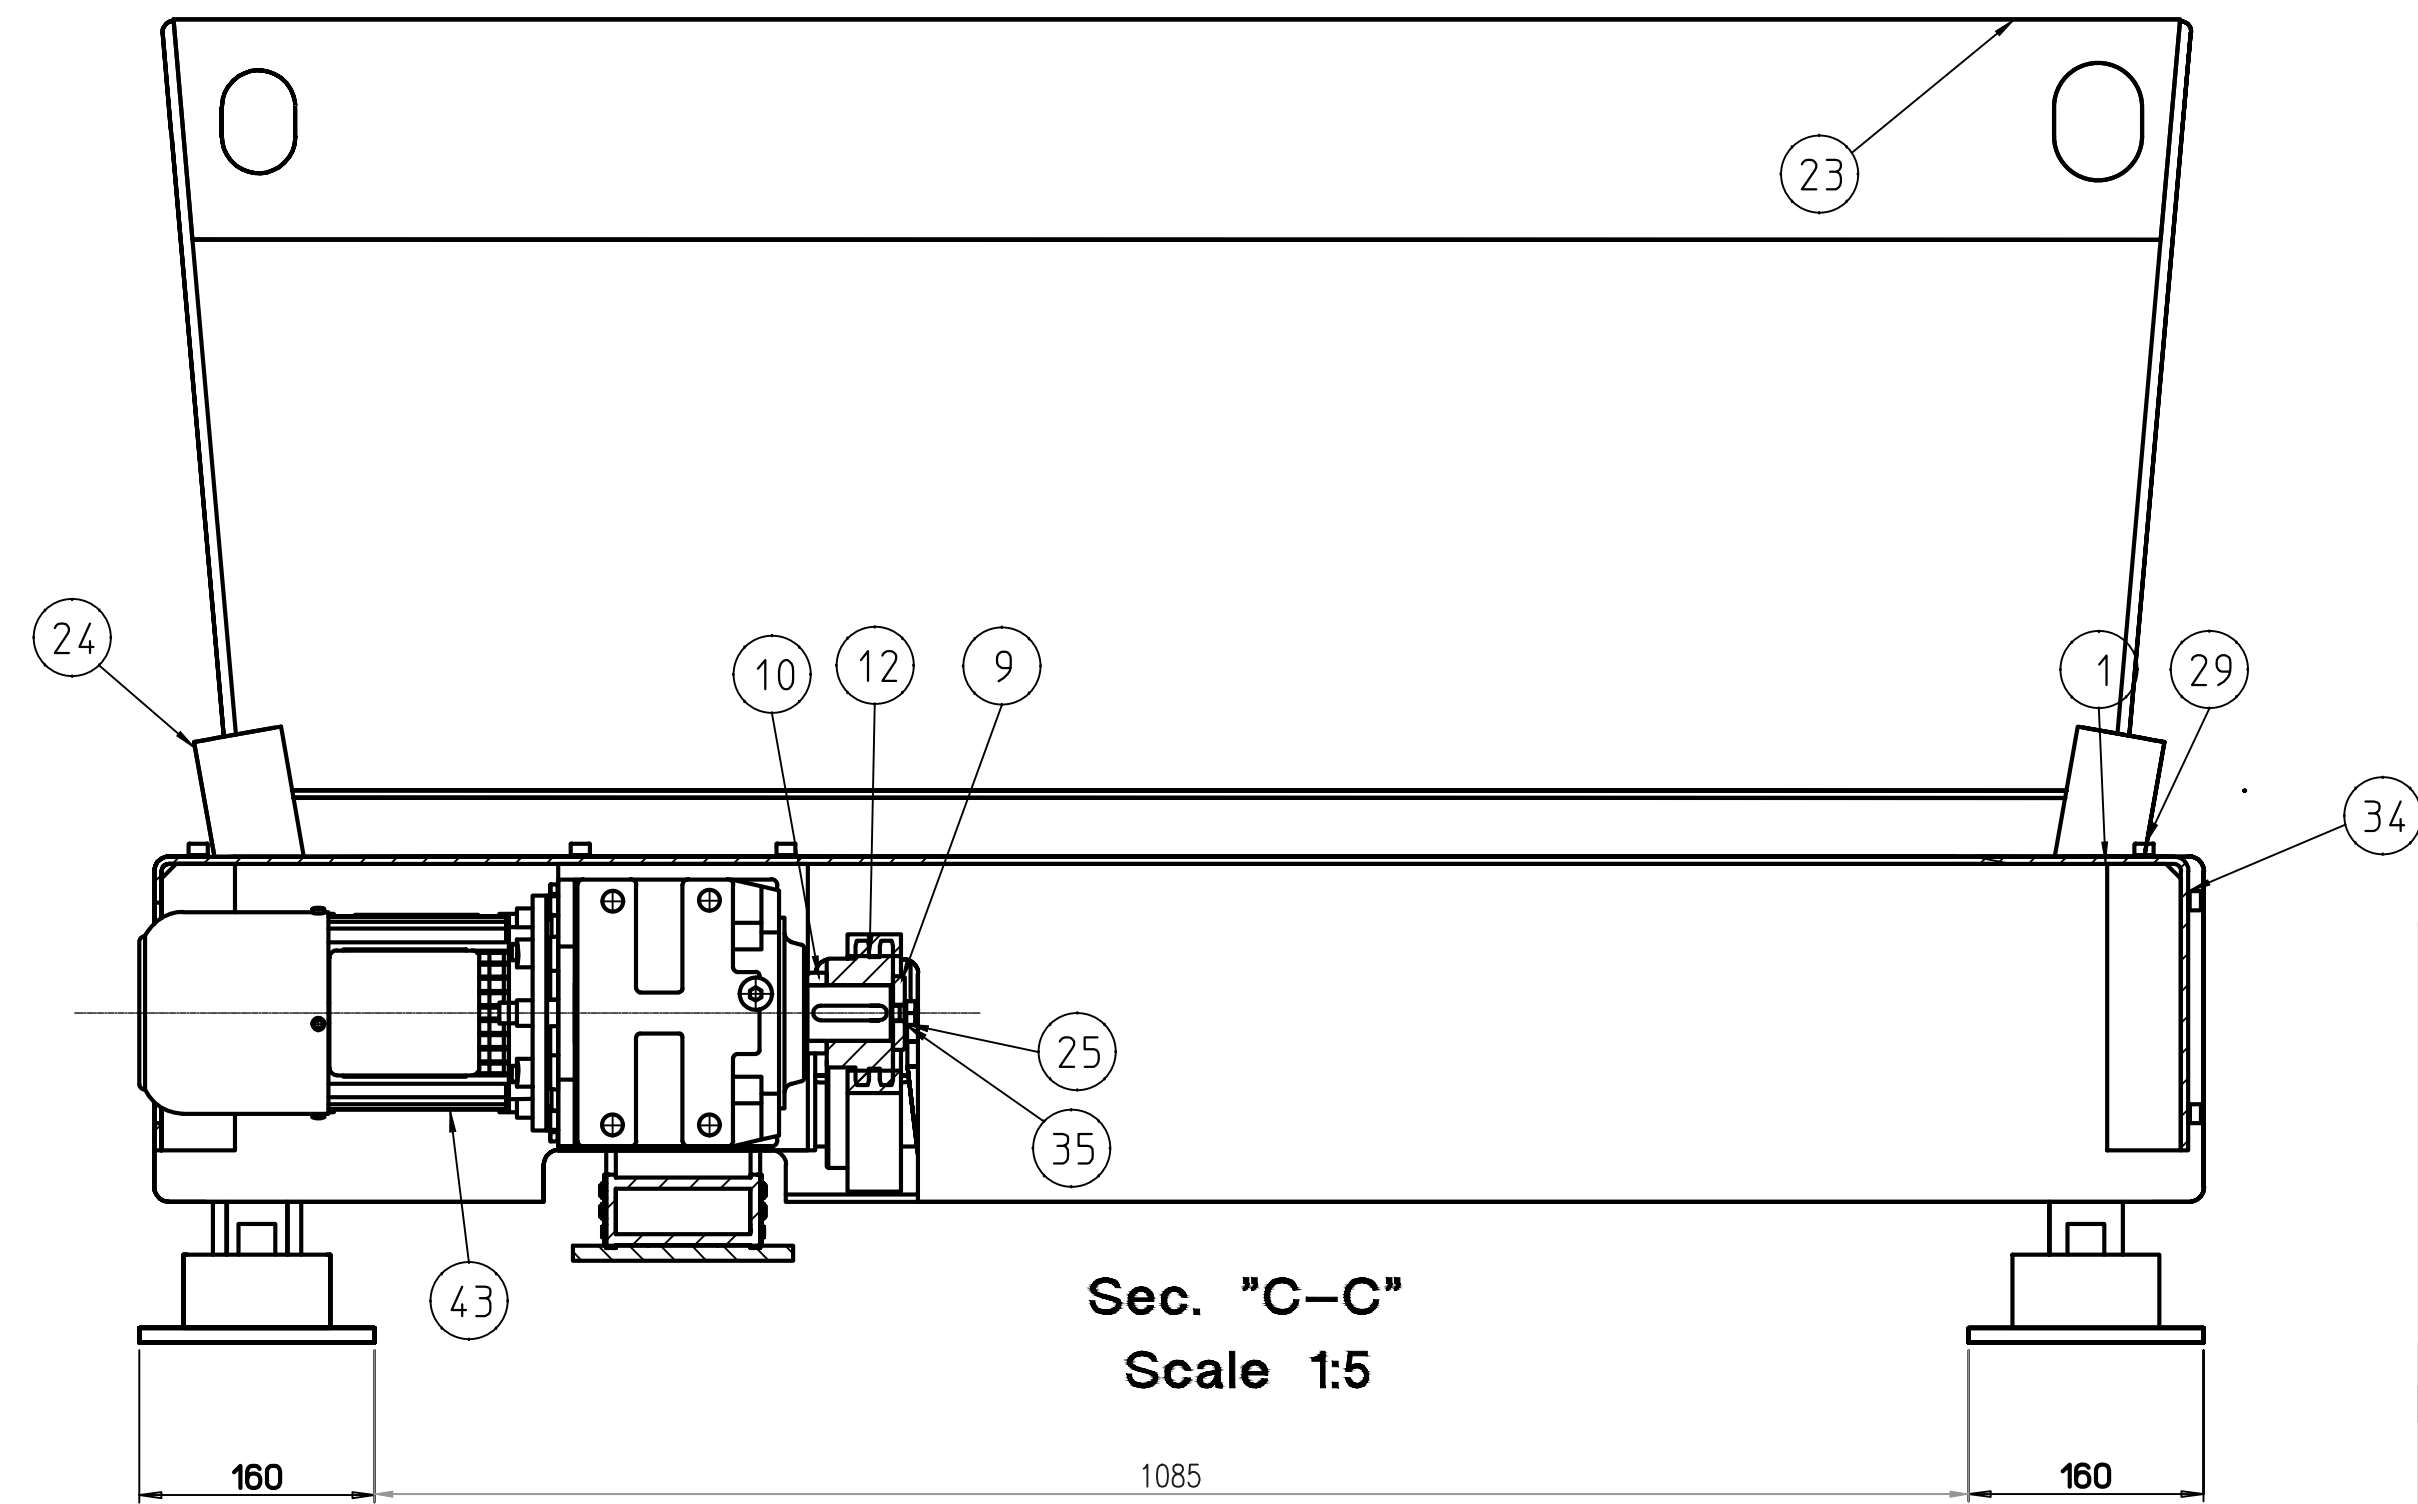


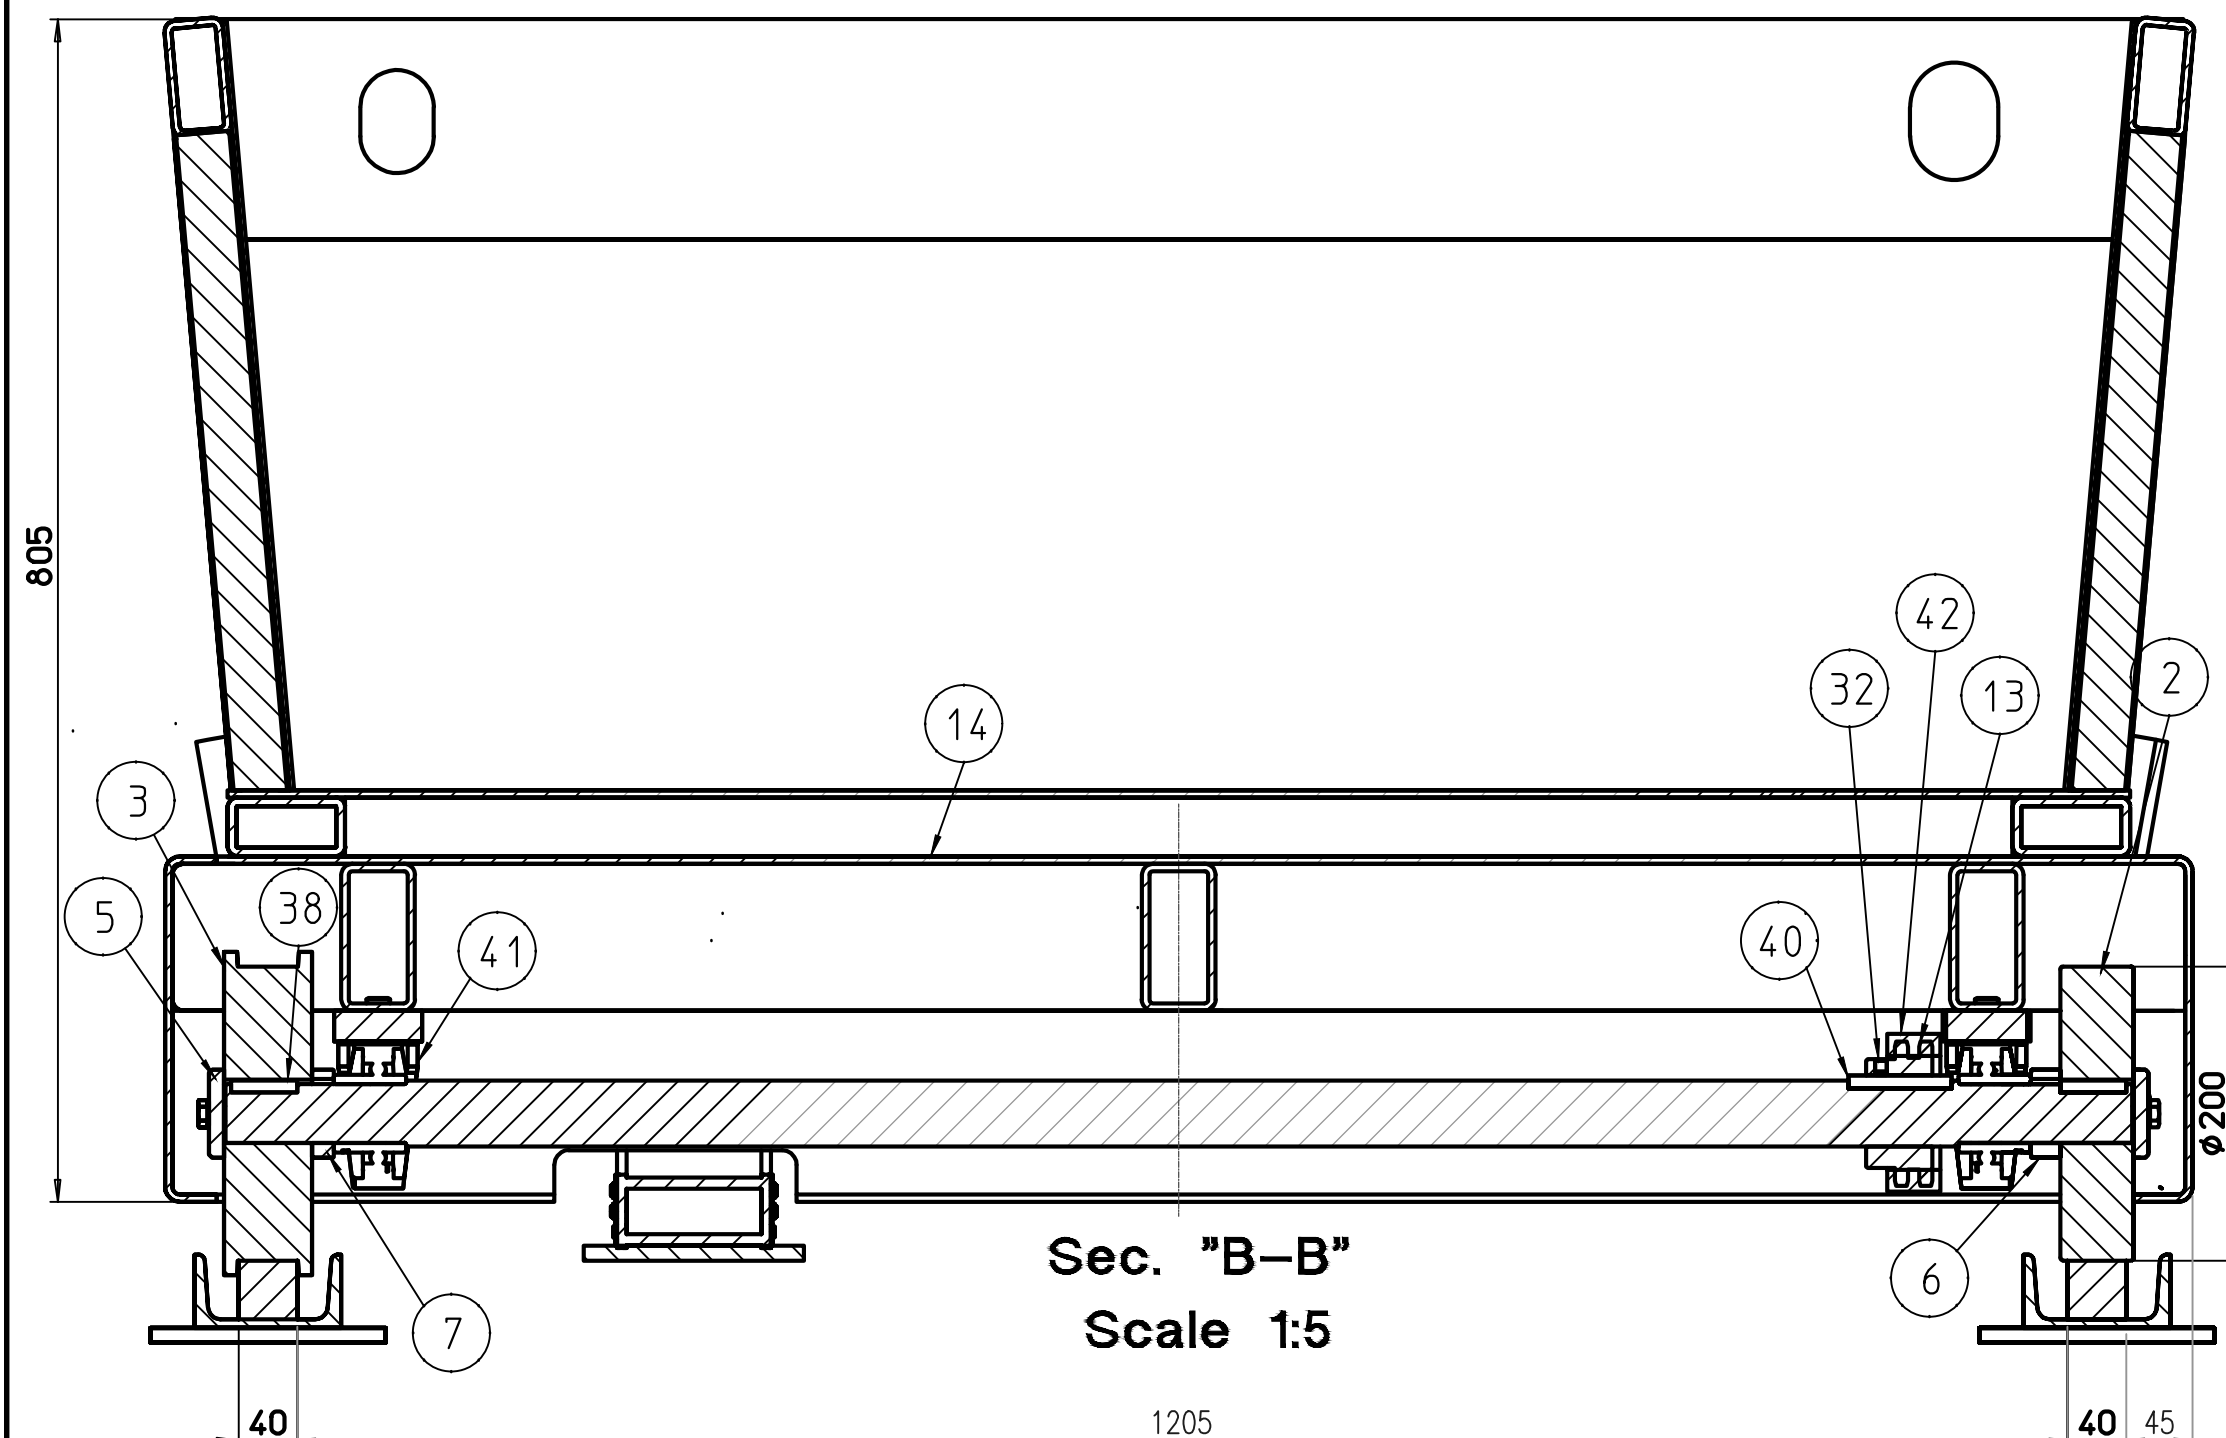

THIS IS THE CONCEPTUAL DRAWING
NOT FOR MANUFACTURING

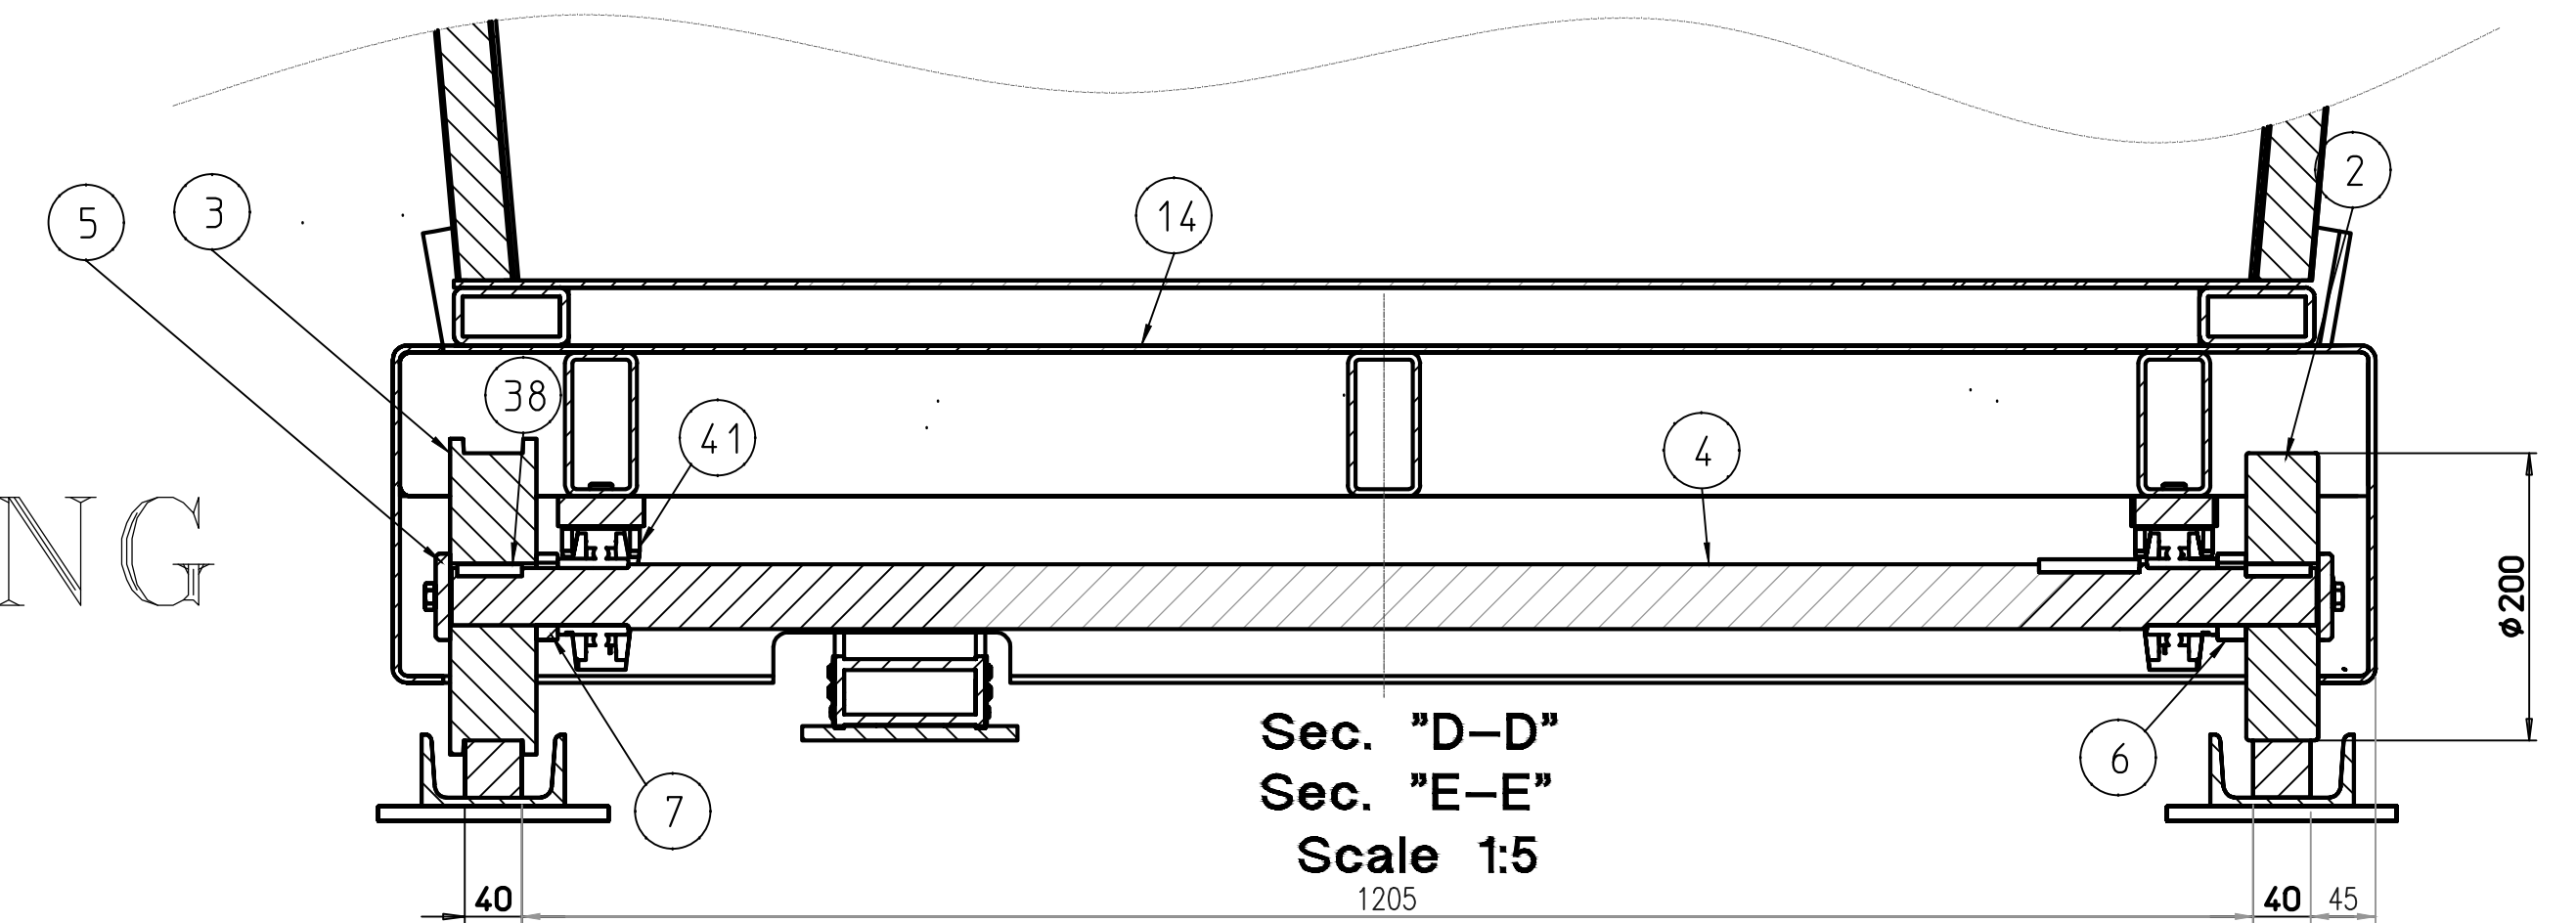

CHECK
PRINT

Tata Steel Downstream Products Limited Inside Tata Steel Works Kalinga Nagar Industrial Complex									
DEVELOPED BY: SMART ENGINEERS & SUPPLIERS SAMARAIPUR BHADRAK									
TITLE		CR PLANT							
DRAWING DESCRIPTION		SLITTER EXIT SCRAP CAR							
SCALE	1:5			MATERIAL MENTIONED IN DETAIL DRAWINGS		WEIGHT IN KG	SHEET 10F 1	SHEET SIZE A1	
DRN.	C.S	01.07.26				---			
CHD.	S.P	01.07.26		DRG NO.		TSDPL-SES-030			
APP.	-	-					REV 0		